


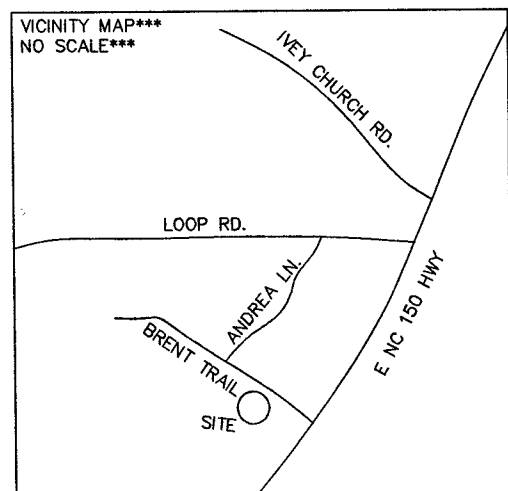

LEGEND

E.I.P. = EXISTING IRON FOUND
I.P.S. = #4 REBAR SET
R/W = RIGHT-OF-WAY
CP = COMPUTED POINT

PARCEL#: 01609
HAMPTONS WRECKER
SERVICE INC
2654/723

PARCEL#: 51024
JULIE M. SPAKE
LC105/590

PARCEL#: 28005
GARY HAWKINS
LC106/630

PARCEL#: 28061
STEPHANIE C. FALLS
2683/687

PARCEL#: 28900
(6.08 AC. TOTAL)



PARCEL#: 51007
JULIE M. SPAKE
LC105/590

SURVEYORS CERTIFICATION


I, WILLIAM M. ALLEN CERTIFY THAT THIS MAP WAS DRAWN UNDER MY SUPERVISION FROM AN ACTUAL SURVEY MADE UNDER MY SUPERVISION DEED DESCRIPTION RECORDED IN BOOK 1655, PAGE 704; THAT THE RATIO OF PRECISION AS CALCULATED BY LATITUDES AND DEPARTURES IS 1:10000, (THAT THE BOUNDARIES NOT SURVEYED ARE SHOWN AS BROKEN LINES PLOTTED FROM INFORMATION FOUND IN BOOK _____, PAGE _____); THAT THIS MAP WAS PREPARED IN ACCORDANCE WITH G.S. 47-30, AS AMENDED.

WITNESS MY HAND AND SEAL THIS 3RD DAY OF MAY, A.D. 2023.

OFFICIAL SEAL OF NORTH CAROLINA
PROFESSIONAL LAND SURVEYOR
WILLIAM M. ALLEN
SEAL
L-3499
REGISTRATION NUMBER

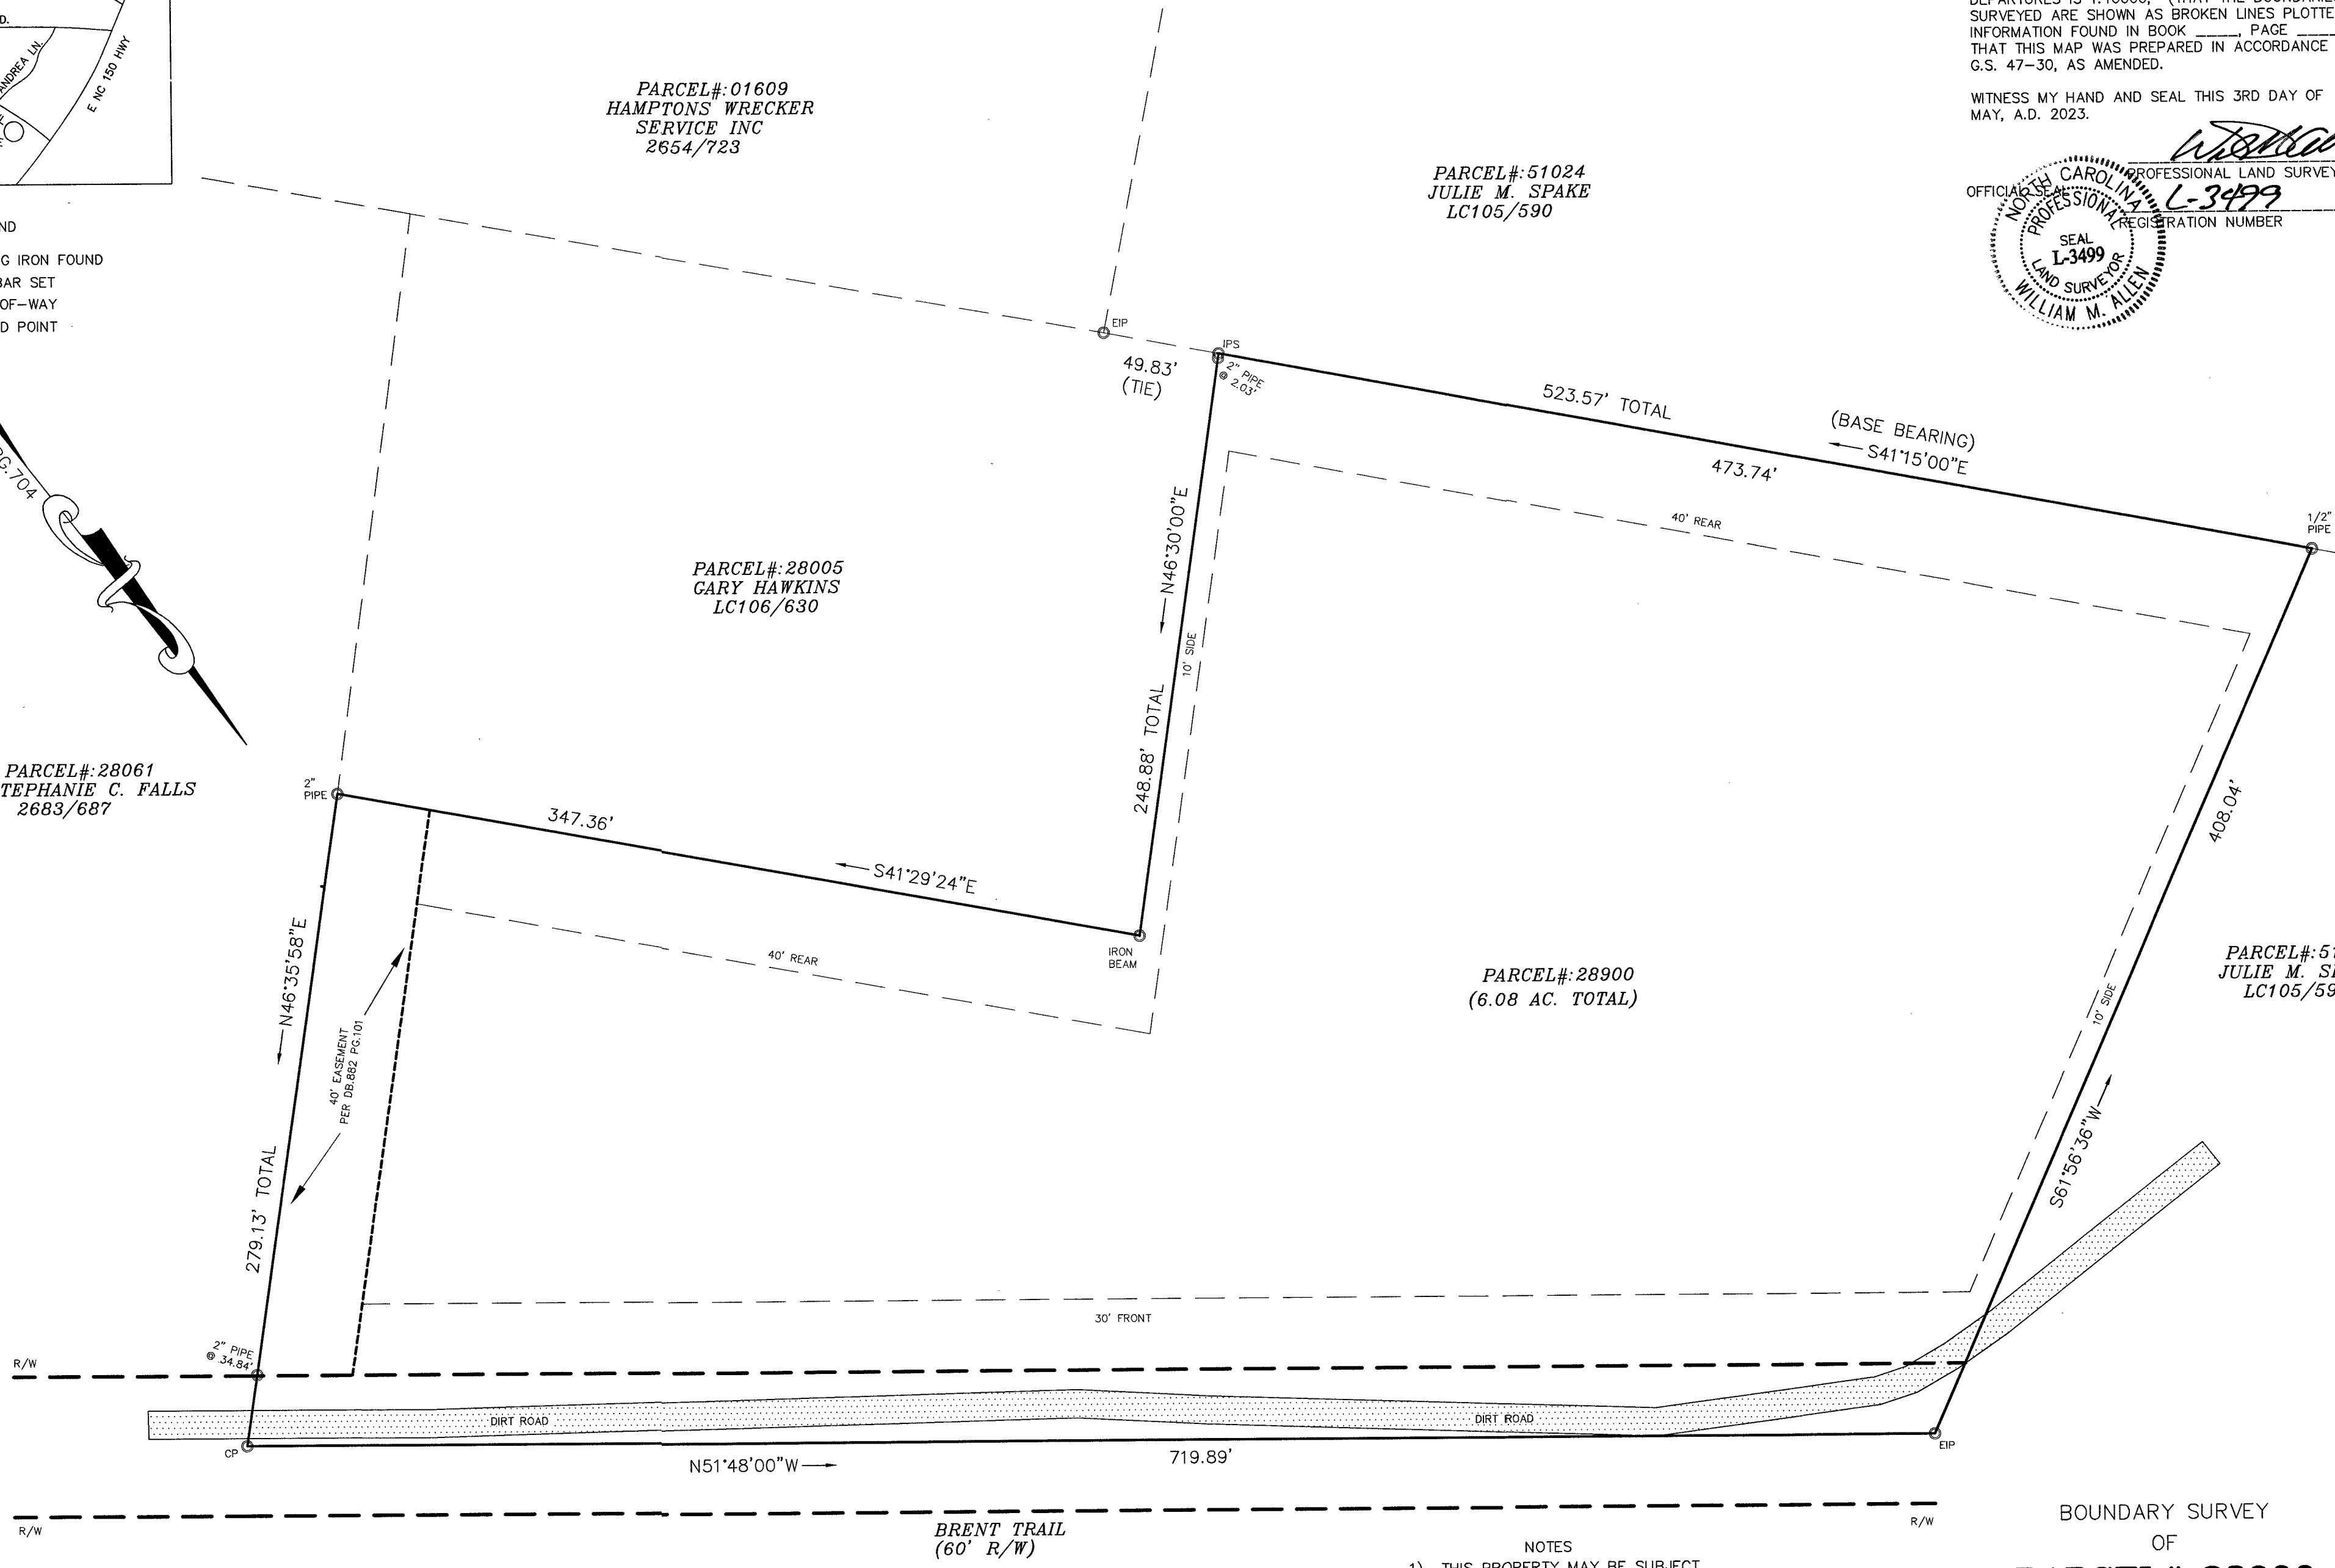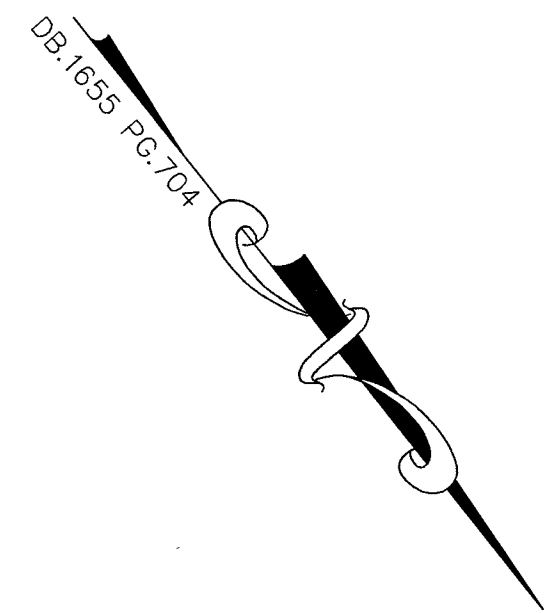

DAS
DON ALLEN & ASSOCIATES P.A.
"Since 1971"
Commercial * Residential * Mortgage Surveys * Multi-Family
Construction Staking * Subdivision Design * Topographical
127 Promenade Drive - Suite E * Mooresville * NC * 28117
(704) 664-7029 (704) 664-8041 Fax
donallensurvey@gmail.com

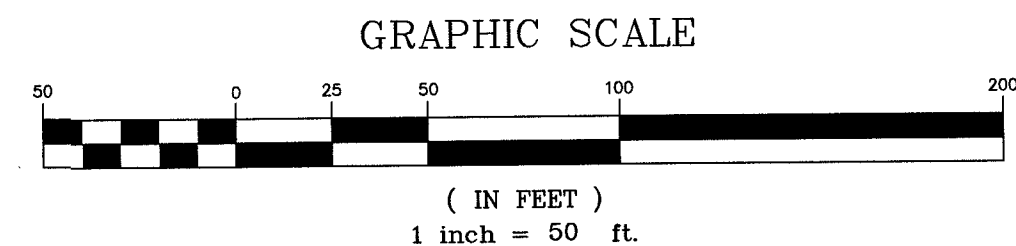

- NOTES
- 1) THIS PROPERTY MAY BE SUBJECT TO ANY EASEMENTS AND/OR RIGHTS OF WAY OF RECORD.
 - 2) ACREAGE COMPUTED BY THE COORDINATE METHOD.
 - 3) UNDERGROUND POWER
 - 4) NO GRID MONUMENT FOUND WITHIN 2000 FEET.
 - 5) DEED REFERENCE: 1655/704
 - 6) TAX PARCEL: 28900
 - 7) ADDRESS: BRENT TRAIL
 - 8) SETBACKS SHOWN PER ZONING PROPERTY ZONED: LINCOLN CO. R-S (VERIFY SETBACKS PRIOR TO ANY NEW CONSTRUCTION)

BOUNDARY SURVEY
OF
PARCEL#: 28900
BRENT TRAIL
IRONTON TWP., LINCOLN CO., N.C.
SCALE: 1" = 50' DATE: MAY 3, 2023
ACQUIRED BY: WILLIAM ERICKSON